SƠ ĐỒ BỐ TRÍ CÔNG TRÌNH VÀ LẤY MẪU DỰ KIẾN

MỎ ĐÁ XÂY DỰNG NÚI HUỲNH THUỘC XÃ KIÊN LƯƠNG, TỈNH AN GIANG

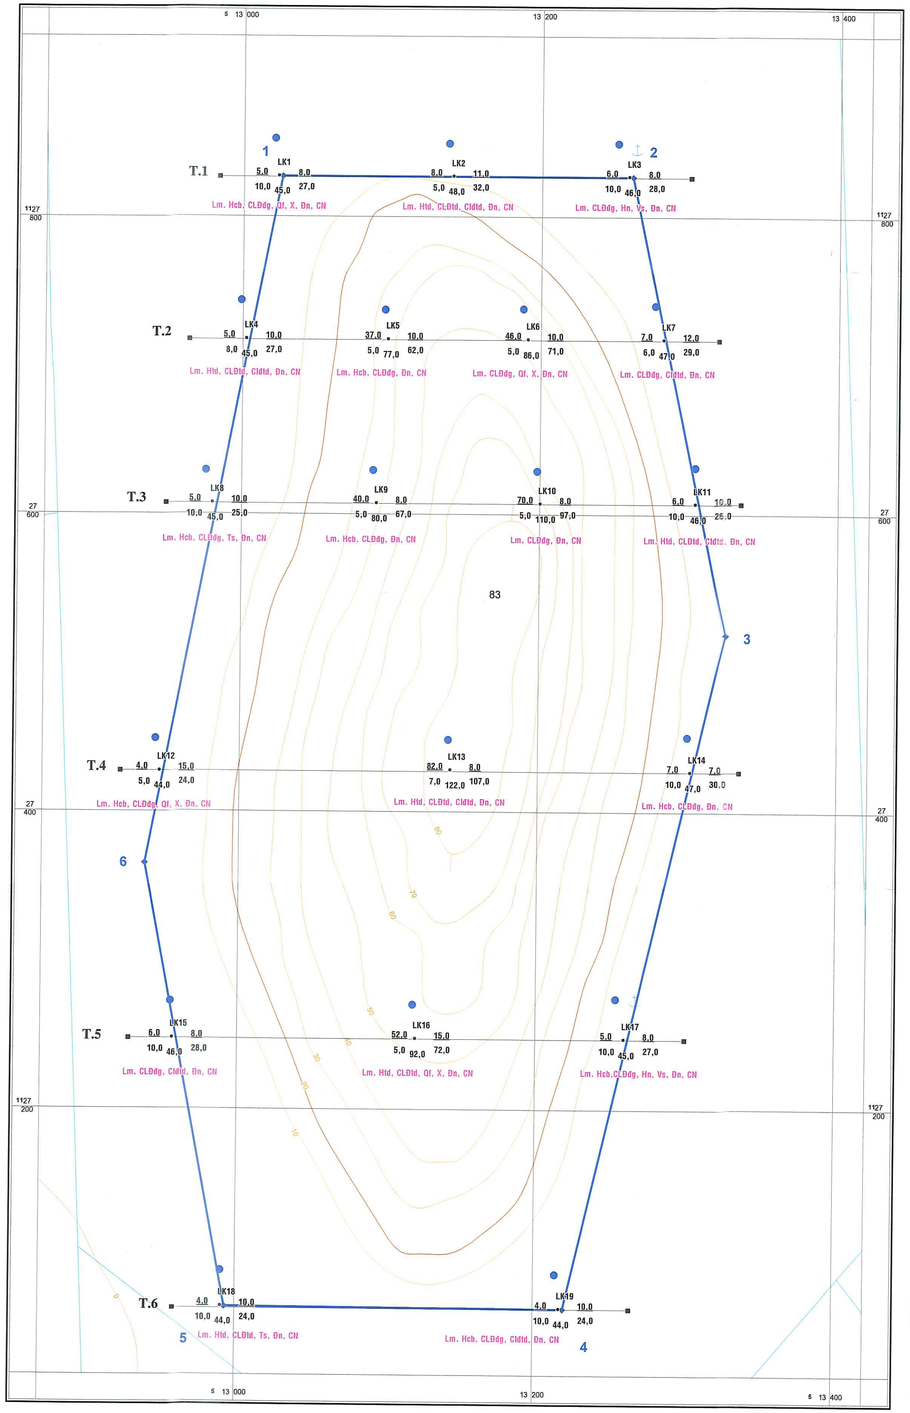

TỶ LỆ 1:2.000

1cm trên bản đồ bằng 20m ngoài thực tế

20 0m 20 40 60 80

CHỈ DẪN

I. CÔNG TRÌNH THĂM DÒ

Lỗ khoan dự kiến thăm dò:
1. Số hiệu;
2. Chiều sâu khoan (m);
3. Cao độ (m);
4. Bề dày lớp phủ (m);
5. Bề dày lớp đá phong hóa (m);
6. Bề dày lớp đá cứng (m).

T.1 — Tuyến thăm dò và số hiệu

II. VỊ TRÍ LẤY MẪU

Lm:	Mẫu lát mỏng
Hfd:	Mẫu hóa toàn diện
Hcb:	Mẫu cơ bản
CLDfd:	Mẫu cơ lý đá toàn diện
CLDđg:	Mẫu cơ lý đá đơn giản
Clđfd:	Mẫu cơ lý đất
Qf:	Mẫu quang phổ
Px:	Mẫu phóng xạ
Ts:	Mẫu trọng sa
Đn:	Mẫu đầm nện (vật liệu san lấp)
Hn:	Mẫu hóa nước
Vs:	Mẫu vi sinh
CN:	Mẫu công nghệ đá xây dựng

Vị trí bơm nước thí nghiệm

Vị trí quan trắc mực nước lỗ khoan

III. CÁC KÍ HIỆU KHÁC

Ranh giới diện tích thăm dò và số hiệu điểm góc

Điểm độ cao và giá trị (m)

Đường bình độ và giá trị (m)

Kênh mương

Lưới tọa độ VN2000, Kinh thuyến trục 104°30', múi 3°

CÔNG TY CỔ PHẦN KHOÁNG SẢN THUẬN PHONG		
ĐỀ ÁN THĂM DÒ KHOÁNG SẢN MỎ ĐÁ XÂY DỰNG TẠI KHU VỰC NÚI HUỲNH THUỘC XÃ KIÊN LƯƠNG, TỈNH AN GIANG		
Bản vẽ số: 04	Tỷ lệ 1:2.000	Năm 2025
Tên bản vẽ: SƠ ĐỒ BỐ TRÍ CÔNG TRÌNH VÀ LẤY MẪU DỰ KIẾN		
Chức danh	Họ và tên	Ký tên
Người thành lập	Nguyễn Thị Ninh Thanh	
Người kiểm tra Chủ biên	Nguyễn Tiến Dũng	
CHỦ ĐẦU TƯ	CƠ QUAN TƯ VẤN	
CÔNG TY CỔ PHẦN KHOÁNG SẢN THUẬN PHONG — Trần Văn Bền	CÔNG TY TNHH MÔI TRƯỜNG VÀ TÀI NGUYÊN MINH ĐỨC — PHÓ GIÁM ĐỐC — Đoàn Ngọc Tài	