BẢN ĐỒ ĐỊA CHẤT, BỐ TRÍ CÔNG TRÌNH VÀ LẤY MẪU

MỎ ĐÁ XÂY DỰNG NÚI DÀI, XÃ Ô LÂM VÀ XÃ TRI TÔN, TỈNH AN GIANG

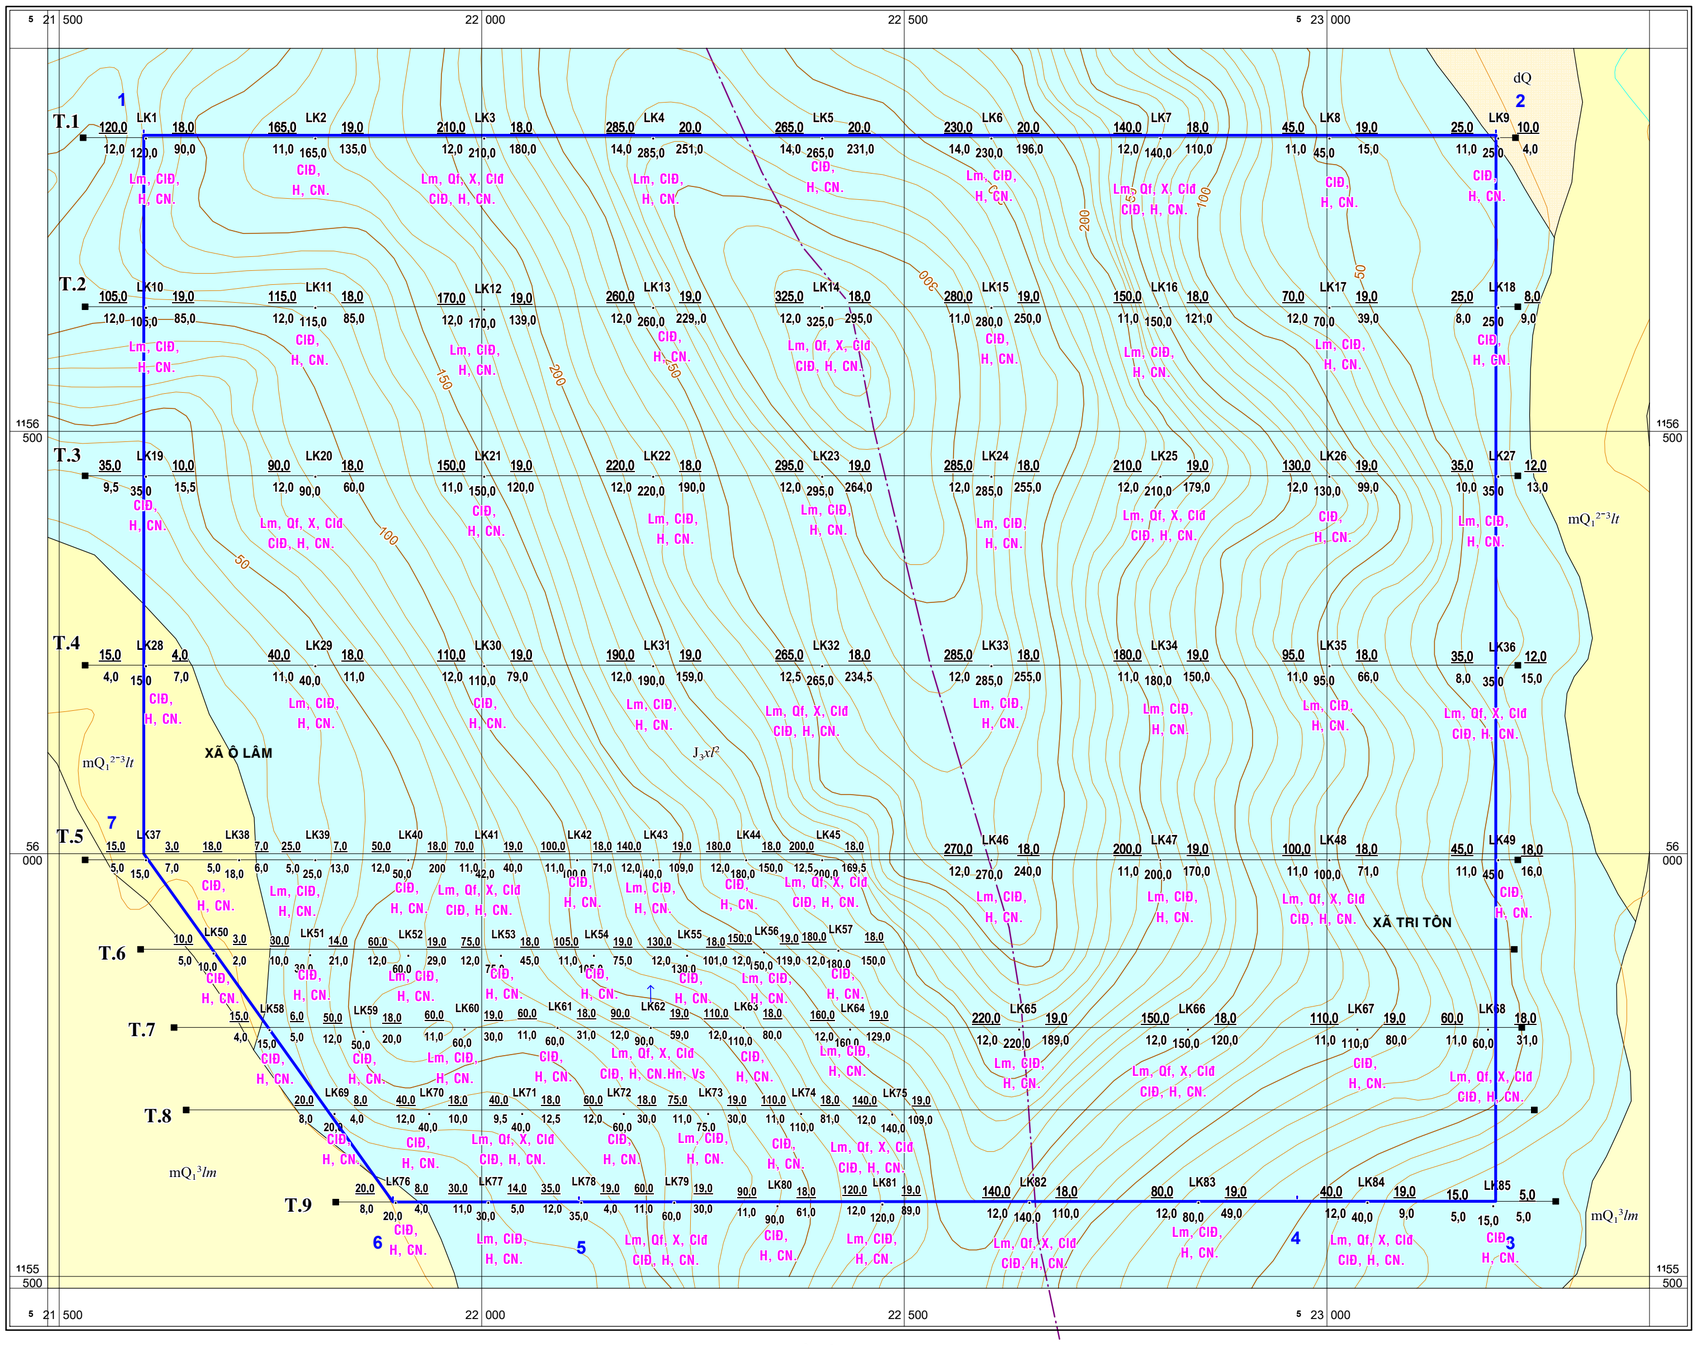

TỶ LỆ 1:5.000

1cm trên bản đồ bằng 50m ngoài thực tế

MẶT ĐỊA CHẤT THEO CÁC TUYẾN T.1 VÀ T.5

TỶ LỆ 1: 5.000

TUYẾN T.1

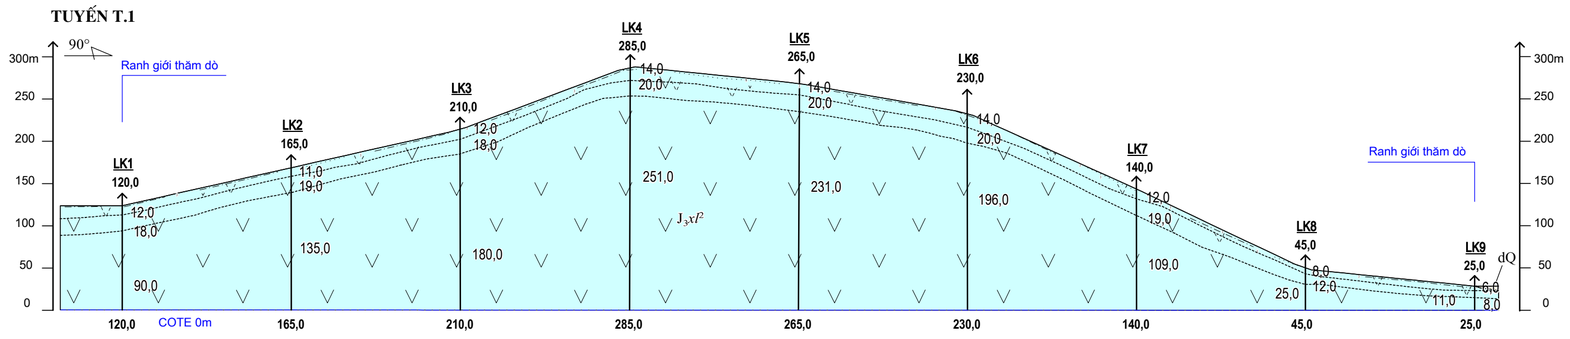

TUYẾN T.5

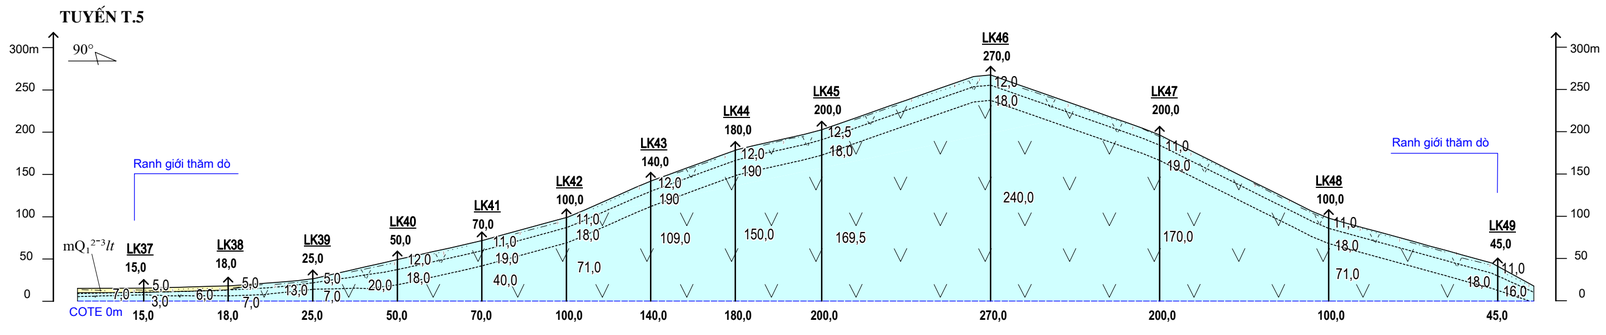

CHỈ DẪN

I. ĐỊA CHẤT

- dQ — Hệ Đệ tứ, không phân chia, trầm tích deluvi (dQ): Dăm, tảng, mảnh vụn, bột sét
- $mQ_1^{2-3}lt$ — Thống Pleistocen, phụ thống trung- thượng, trầm tích biển. Hệ tầng Long Toàn: Cát, cuội, sỏi, bột sét. Dày 5-20m.
- mQ_1^3lm — Thống Pleistocen, phụ thống thượng, trầm tích biển. Hệ tầng Long Mỹ: Cát, cát bột, sét bột màu xám vàng. Dày 10-50m.
- J_3xl^2 — Hệ Jura, thống thượng. Hệ tầng Xà Lôn: Tập 2. Cuội kết, cát kết, cát sạn kết, sét silic, bột kết màu tím, tuf andesit, andesitobazan, felsit, ryolit. Dày >200m.
- Ranh giới địa chất

II. CÔNG TRÌNH

Lỗ khoan dự kiến thăm dò:

1. Số hiệu lỗ khoan;
2. Chiều sâu khoan (m);
3. Cao độ lỗ khoan (m);
4. Bề dày lớp phủ (m);
5. Bề dày lớp bán phong hóa (m);
6. Bề dày lớp đá cứng (m).

T.4 — Tuyến công trình và số hiệu

Vị trí bơm nước thí nghiệm

III. LẤY MẪU

Các loại mẫu lấy phân tích:

- Lm: Mẫu lát mỏng
- Qf: Mẫu quang phổ
- X: Mẫu tham số phóng xạ
- Cld: Mẫu cơ lý đất
- CID: Mẫu cơ lý đá
- H: Mẫu hoá
- CN: Mẫu công nghệ (mài mòn, bám dình..)
- Hn: Mẫu hóa nước
- Vs: Mẫu vi sinh

IV. THẠCH HỌC

Kí hiệu thạch học:

- Cát lẫn sạn sỏi, dăm sạn
- Bột sét
- Đá bán phong hóa
- Andesit

Kí hiệu lỗ khoan trên mặt cắt:

1. Số hiệu lỗ khoan;
2. Chiều sâu khoan (m);
3. Cao độ lỗ khoan (m);
4. Bề dày lớp phủ (m);
5. Bề dày lớp bán phong hóa (m);
6. Bề dày lớp đá cứng (m).

- 90° — Phương vị mặt cắt
- Ranh giới thạch học
- Ranh giới địa chất

V. CÁC KÍ HIỆU KHÁC

- Ranh giới thăm dò và số hiệu điểm góc
- 342 — Điểm độ cao và giá trị (m)
- 50 — Đường bình độ và giá trị (m)
- Sông suối
- Ranh hành chính xã
- Lưới tọa độ VN2000 An Giang, múi 3

CÔNG TY TNHH KHOÁNG SẢN THUẬN PHONG		
ĐỀ ÁN THĂM DÒ MỎ ĐÁ XÂY DỰNG NÚI DÀI XÃ Ô LÂM VÀ XÃ TRI TÔN, TỈNH AN GIANG		
Bản vẽ số: 04	Tỷ lệ 1: 5.000	Năm 2025
BẢN ĐỒ ĐỊA CHẤT, BỐ TRÍ CÔNG TRÌNH VÀ LẤY MẪU		
Chức danh	Họ và tên	Kí tên
Người thành lập	Nguyễn Thị Ninh Thanh	
Người kiểm tra	Nguyễn Tiến Dũng	
Chủ nhiệm		
CHỦ ĐẦU TƯ CÔNG TY TNHH KHOÁNG SẢN THUẬN PHONG GIÁM ĐỐC	ĐƠN VỊ TƯ VẤN CÔNG TY CỔ PHẦN TƯ VẤN ĐẦU TƯ KHOÁNG SẢN VIỆT GIÁM ĐỐC	