BÌNH ĐỒ HIỆN TRẠNG CÔNG TRÌNH

DỰ ÁN: NẠO VÉT, KHƠI THÔNG DÒNG CHẢY PHỤC VỤ CHO SẢN XUẤT NÔNG NGHIỆP, TRẠM BƠM BẮC RUỘNG, XÃ TÁNH LINH

TL 1/2000

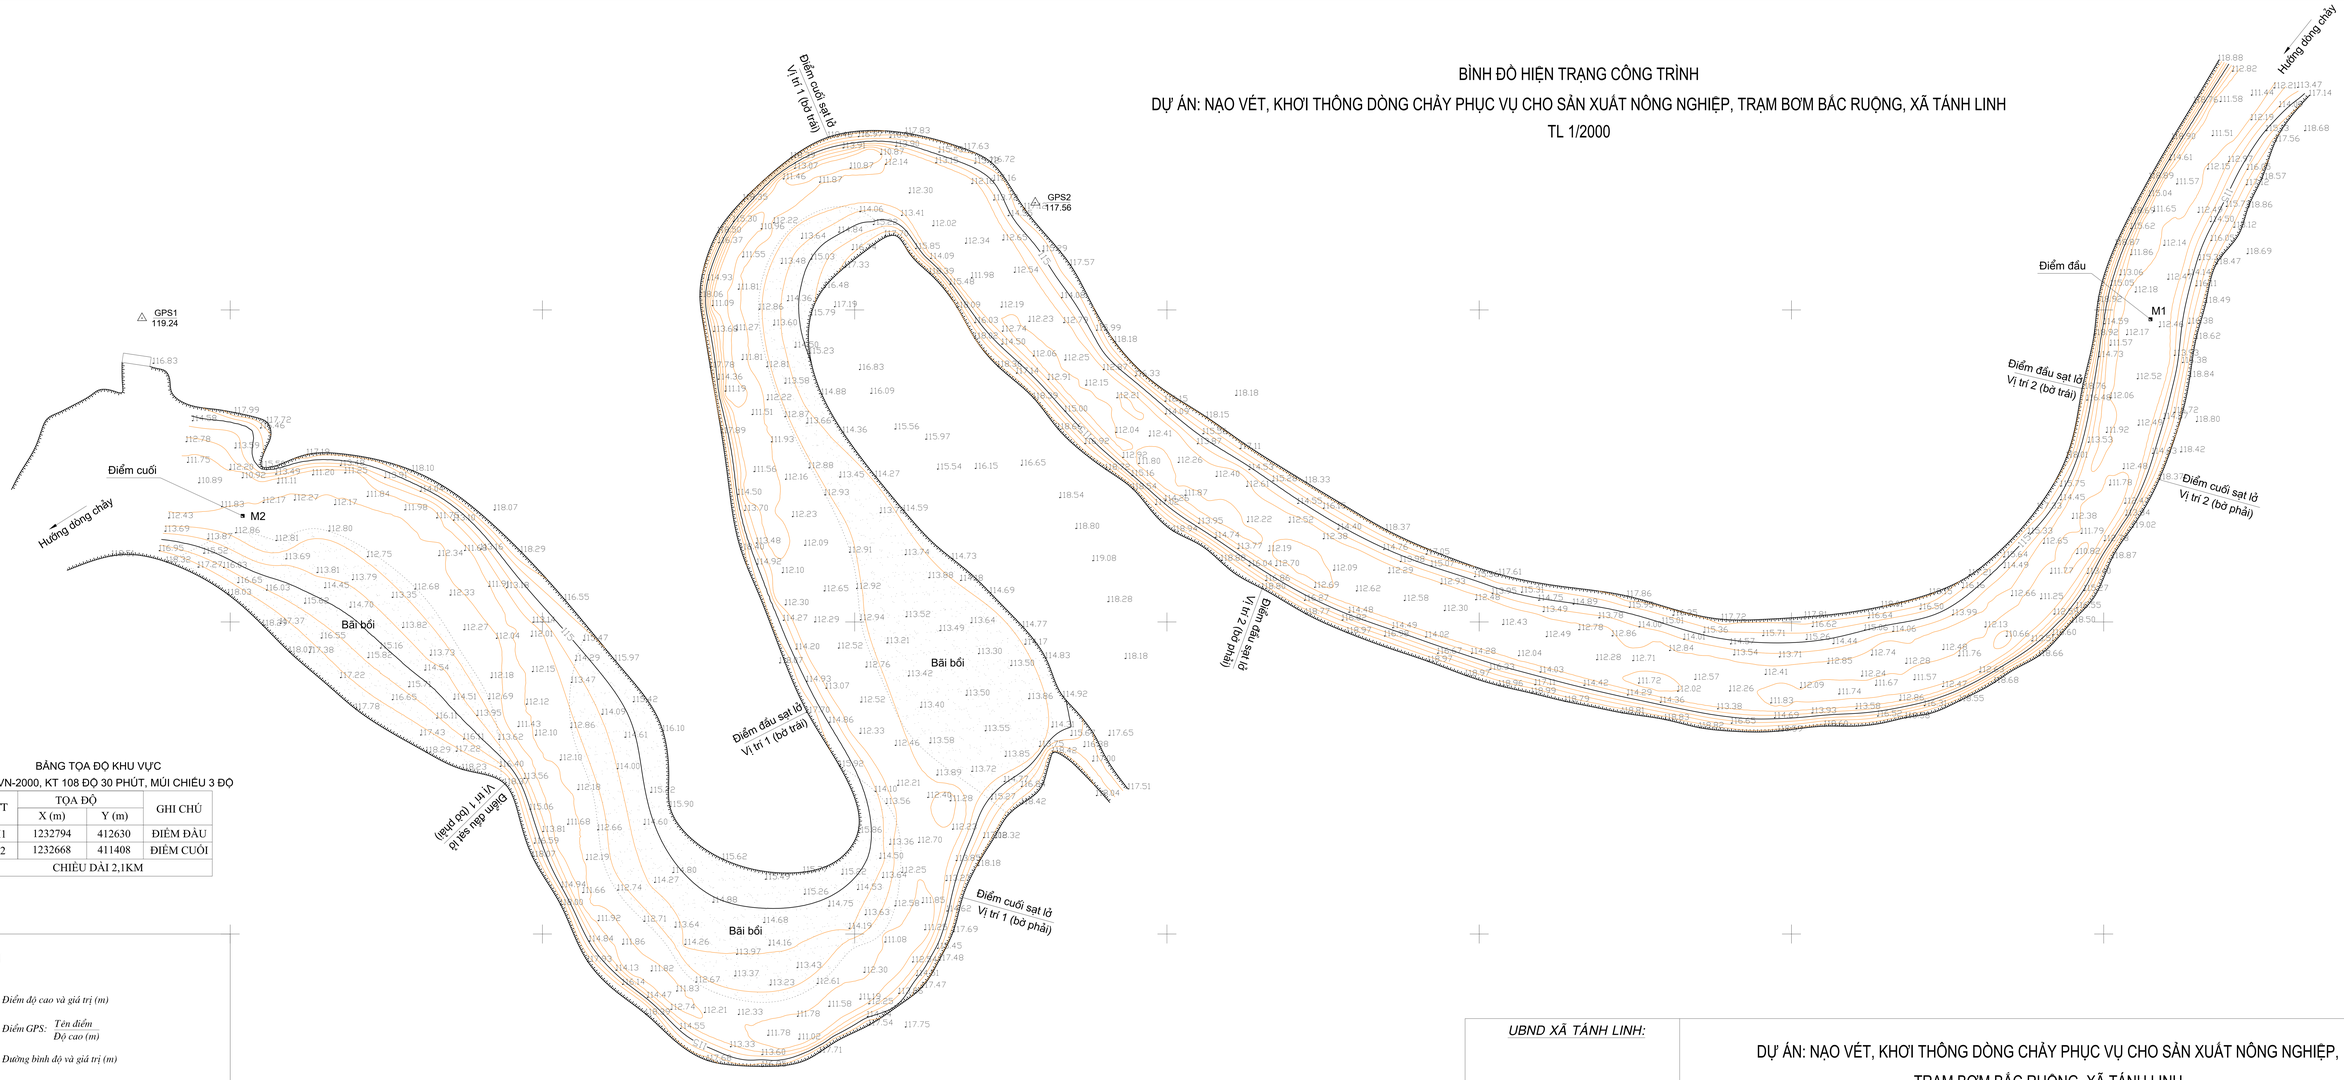

BẢNG TỌA ĐỘ KHU VỰC

HỆ TỌA ĐỘ VN-2000, KT 108 ĐỘ 30 PHÚT, MÚI CHIẾU 3 ĐỘ

STT	TỌA ĐỘ		GHI CHÚ
	X (m)	Y (m)	
M1	1232794	412630	ĐIỂM ĐẦU
M2	1232668	411408	ĐIỂM CUỐI
CHIỀU DÀI 2,1KM			

CHỈ DẪN

- 111.68 — *Điểm độ cao và giá trị (m)*
- GPS1 119.24 — *Điểm GPS: Tên điểm / Độ cao (m)*
- 115 — *Đường bình độ và giá trị (m)*
- *Sông suối*
- *Bãi bồi*

TỶ LỆ 1:2000

1 cm trên bản đồ bằng 20m ngoài thực địa

40m 20 0 40 80 120 160m

UBND XÃ TÁNH LINH:	DỰ ÁN: NẠO VÉT, KHƠI THÔNG DÒNG CHẢY PHỤC VỤ CHO SẢN XUẤT NÔNG NGHIỆP, TRẠM BƠM BẮC RUỘNG, XÃ TÁNH LINH TL 1/2000		
	BÌNH ĐỒ HIỆN TRẠNG CÔNG TRÌNH		
	NĂM 2026	TỶ LỆ 1:2000	BẢN VẼ SỐ: 01

TỜ SỐ